
EV Charging Station Layout

สถานีชาร์จรถยนต์ไฟฟ้า | ถนนสมโภชเชียงใหม่ 700 ปี | เชียงใหม่

พิกัด: 18.7405°N, 98.9632°E | ที่ดิน 5 ไร่ 3 งาน 57 ตรว. (≈9,428 ตรม.)

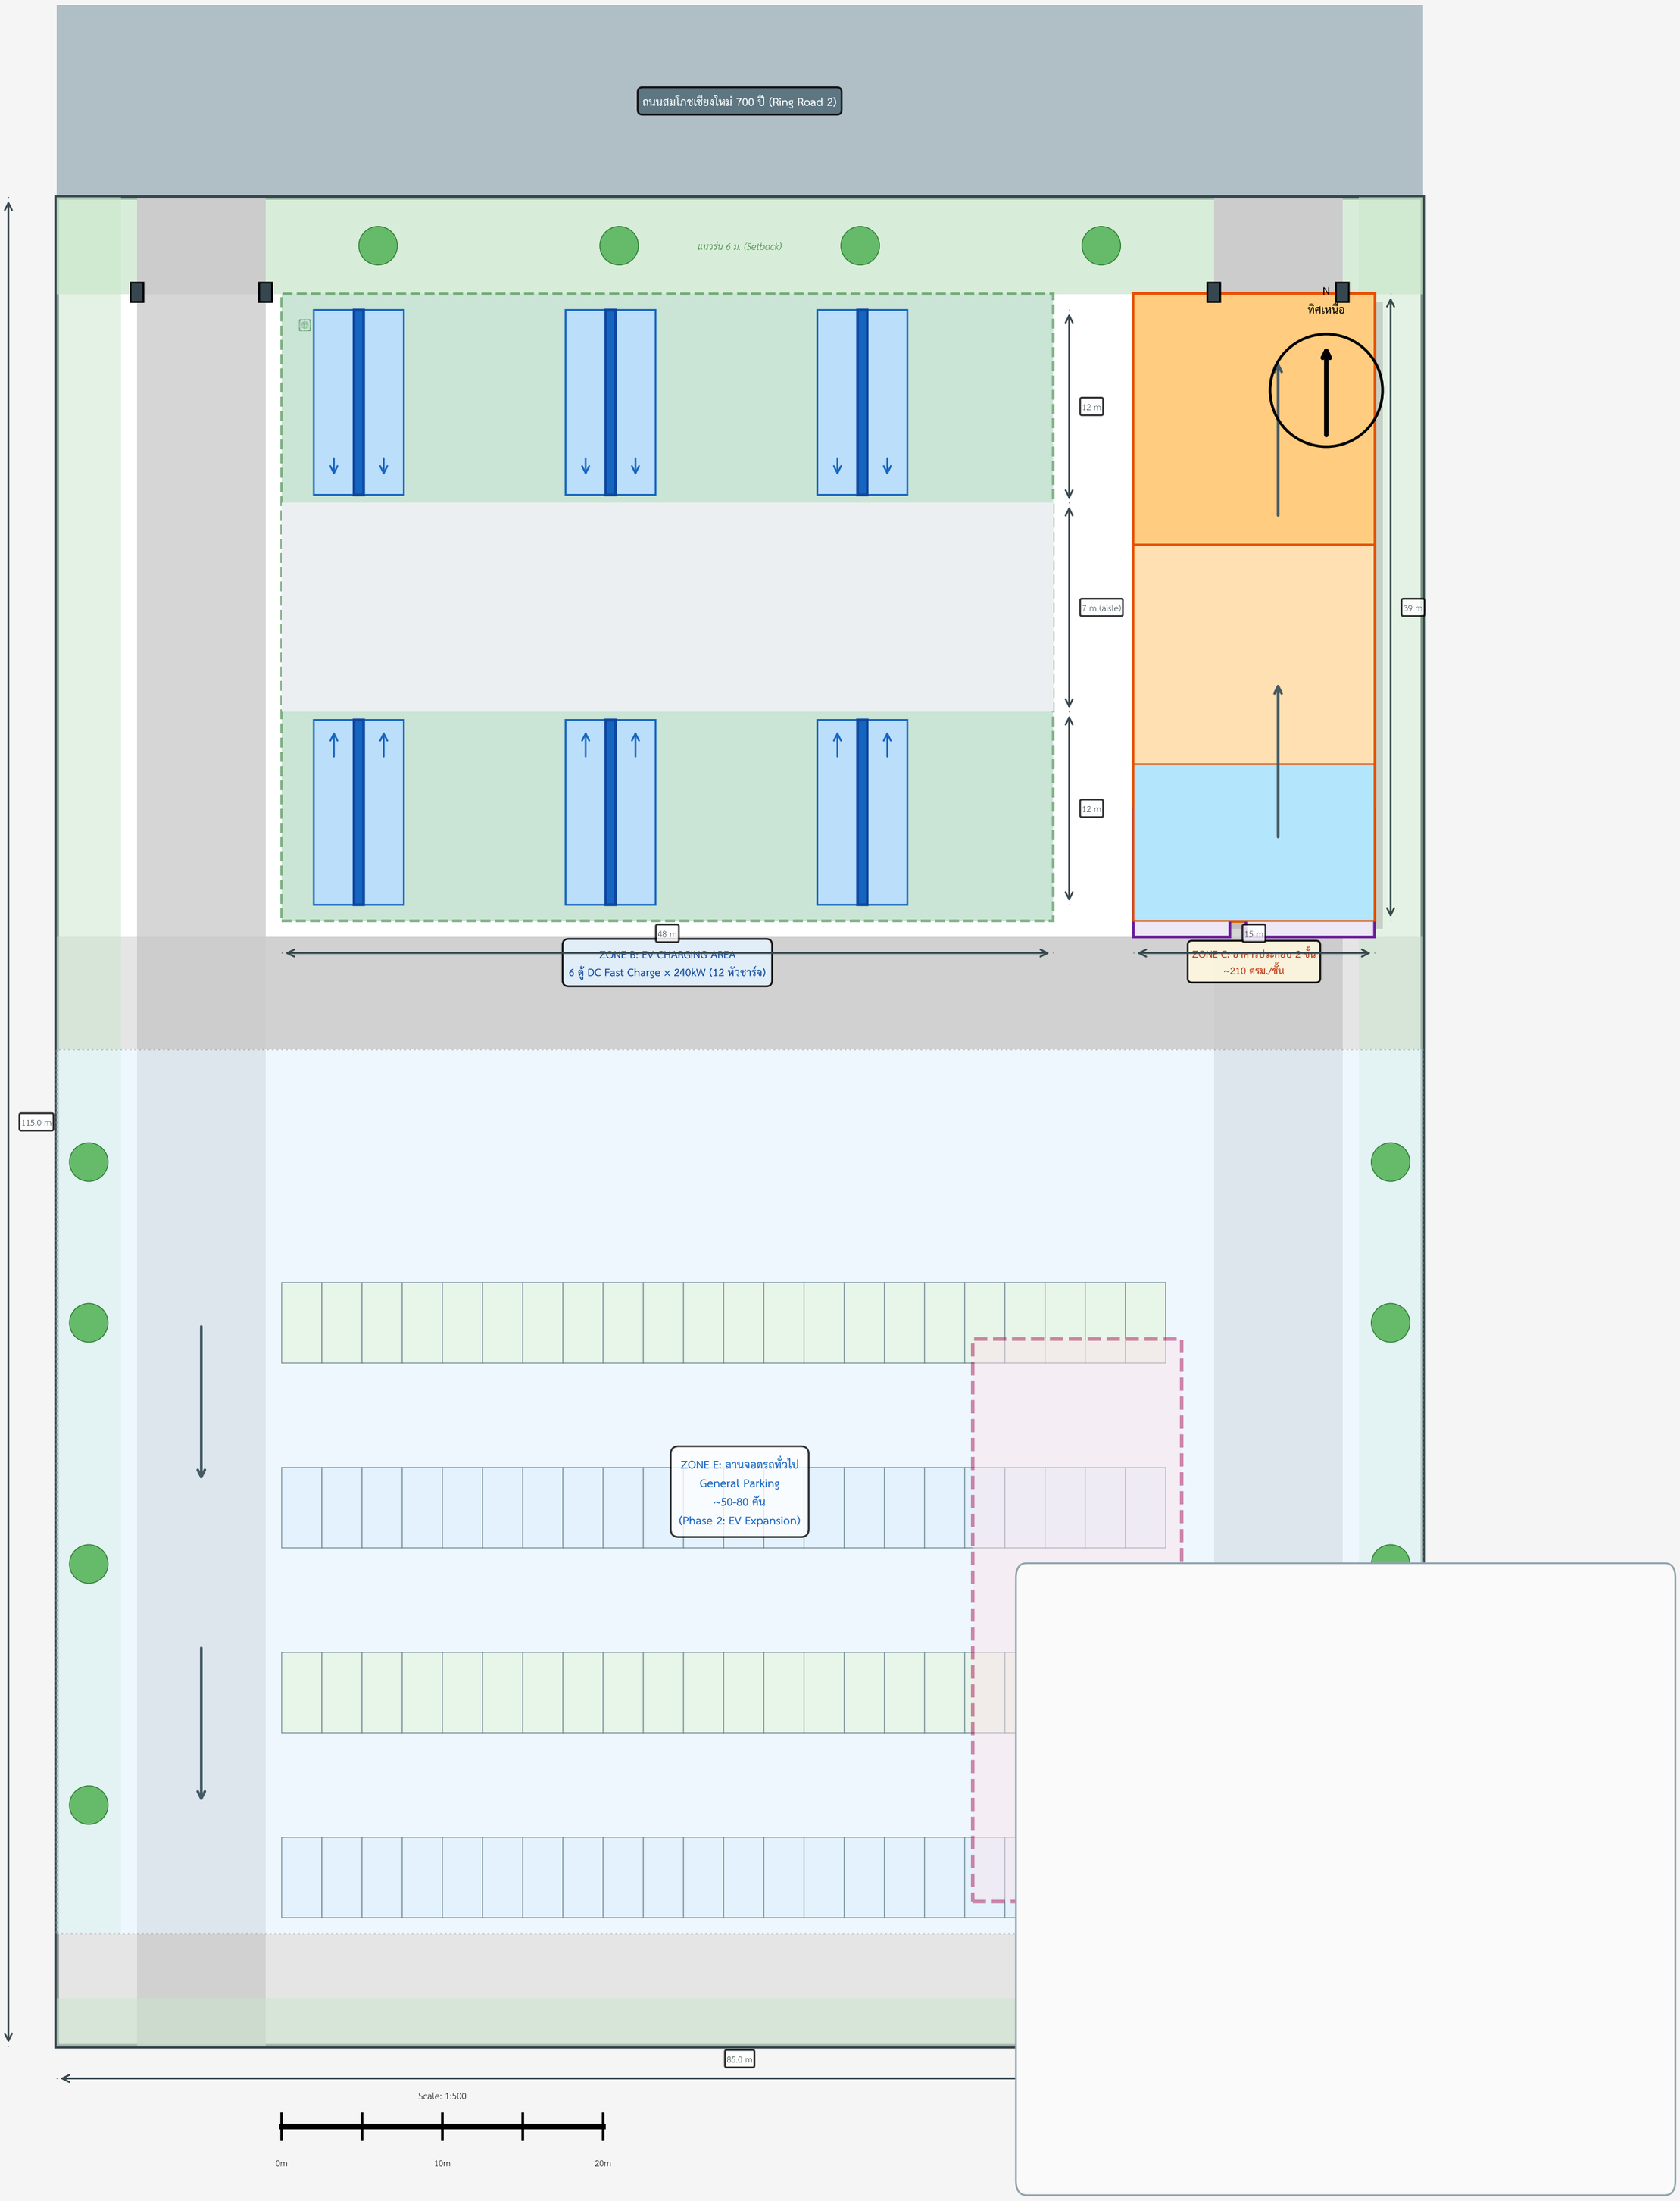

DC Fast Charge: 6 ตู้ × 240 kW × 2 หัวชาร์จ = 12 จุดชาร์จ Phase 1

อาคารประกอบ: ร้านกาแฟ ~90 ตรม. + ร้านค้า ~80 ตรม. + ห้องน้ำ ~40 ตรม.

ออกแบบโดย: ลุงพี AI | วันที่: 24 ต.ค. 2569 | Scale 1:500

EV Charging Station - Design Summary

สรุปการออกแบบ | ถนนสมโภชเชียงใหม่ 700 ปี เชียงใหม่

Zone	รายละเอียด	ขนาด (ตรม.)	หมายเหตุ
A Front Zone	แนวรั่น+ทางเข้า-ออก 2 จุด ป้ายโครงการ+สวนหย่อม	~510	ทางเข้า W=8m DecelerationLane
B EV Charging	DC Fast Charge 6 ตู้×240kW 2 แถว × 3 ตู้ (12 หัวชาร์จ) หลังคา Canopy	~1,440	ช่องชาร์จ: 3.5×6.0m Drive Aisle: 7.0m Phase1=12 หัว
C อาคารประกอบ	ร้านกาแฟ ~90 ตรม. ร้านค้า ~80 ตรม. ห้องน้ำ ~40 ตรม. (2 ชั้น รวม ~420 ตรม.)	~585	สูง 2 ชั้น GFA ~420 ตรม. Balcony ชั้น 2
D Utility	ห้อง MV/LV Transformer EVCS Controller/SCADA	~96	ระบบไฟฟ้าหลัก 2,000kVA
E Parking	ลานจอดรถทั่วไป ถนนภายในโครงการ Two-way	~3,500	~50-80 คัน Phase2 EV Expand
F Green/Future	สวนภูมิทัศน์ พื้นที่สำรองขยาย Phase 2	~3,297	รองรับ +20 EV ช่อง

PHASE 2 EXPANSION: เพิ่มช่องชาร์จได้อีก 10-20 หัวในโซน E (ทิศตะวันออก)
Pre-installed: ร้อยท่อใต้ดิน + ราง Cable Tray เตรียมไว้ Phase 1
Power: ขยาย MV Transformer เพิ่มได้สูงสุด 4,000 kVA

ระบบไฟฟ้า (Electrical System):
- แรงดัน: 22kV ลงมา 400V/230V ผ่าน MV Transformer 2,000 kVA
- ตู้ DC Fast Charge: Phase 1 = 6 ×240kW = 1,440 kW peak (demand ~50-60%)
- UPS/Battery Storage แนะนำ 500kWh สำหรับ peak shaving
- Solar Rooftop บนหลังคา Canopy ~100-150kWp (option)
- ระบบ EVCS Management + Smart Meter + Load Balancing

ออกแบบโดย: ลุงพี AI | วันที่: 24 ต.ค. 2569 | พิกัด: 18.7405°N, 98.9632°E

ระบบจราจร (Traffic Layout - Two-way):
- ทางเข้า (ENTER): ทิศตะวันตก กว้าง 8 ม. + Deceleration Lane 50 ม.
- ทางออก (EXIT): ทิศตะวันออก กว้าง 8 ม.
- ถนนภายใน: Two-way 6 ม. วนรอบโครงการ
- ต้องขออนุญาตกรมทางหลวง (เชื่อมทางหลวงหมายเลข...)